Bonebrake Cover — Drill Map (Rev C, 8.500 x 41.125)

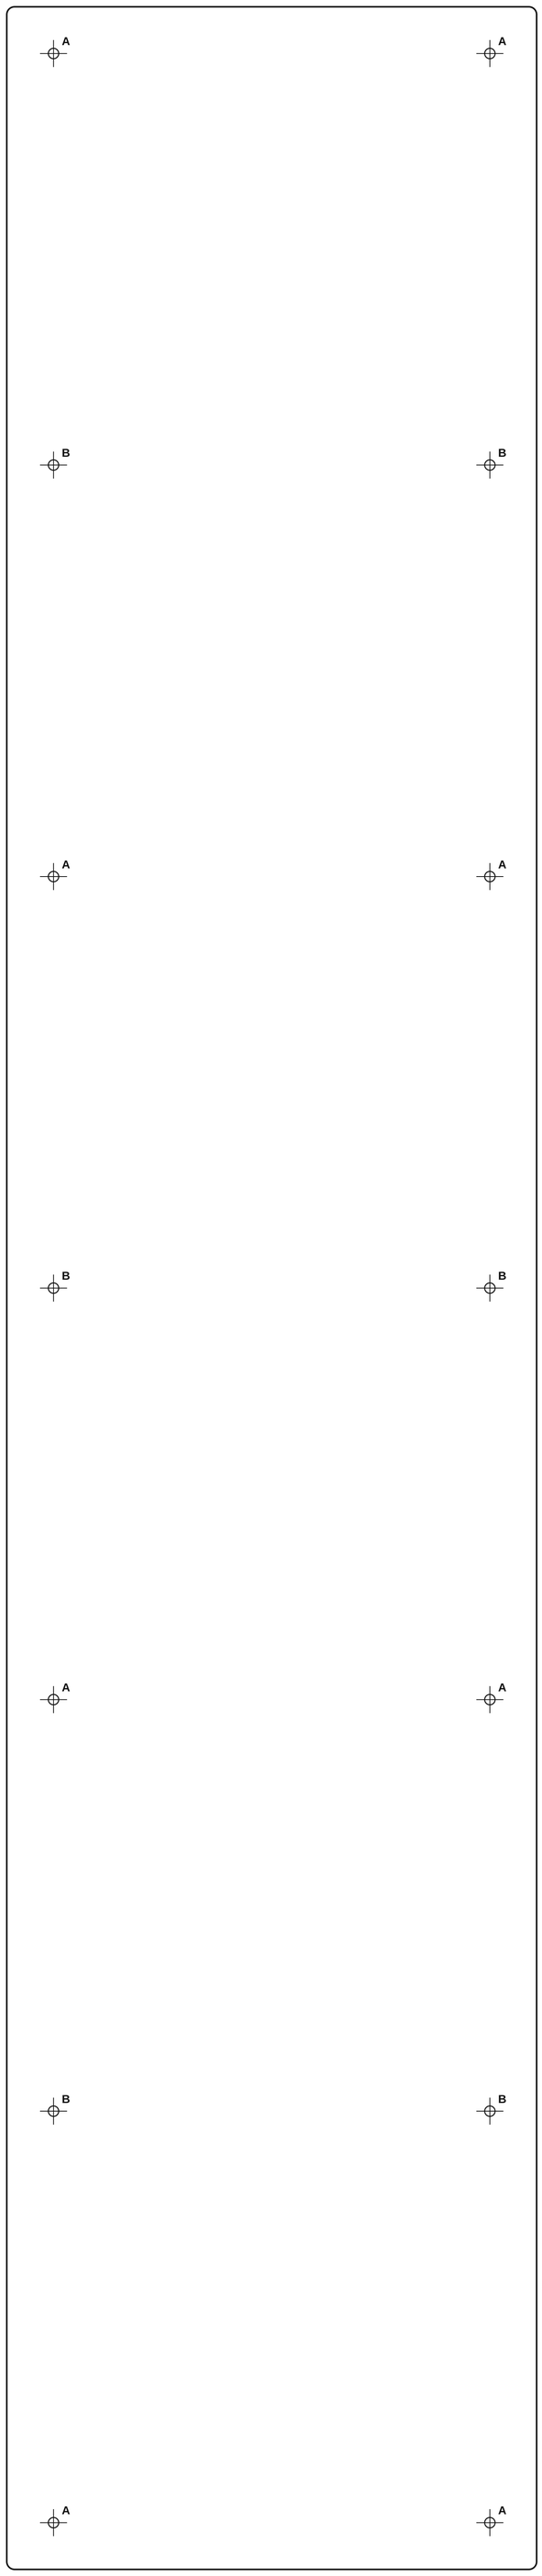

face (art side up) — 8.500" × 41.125"

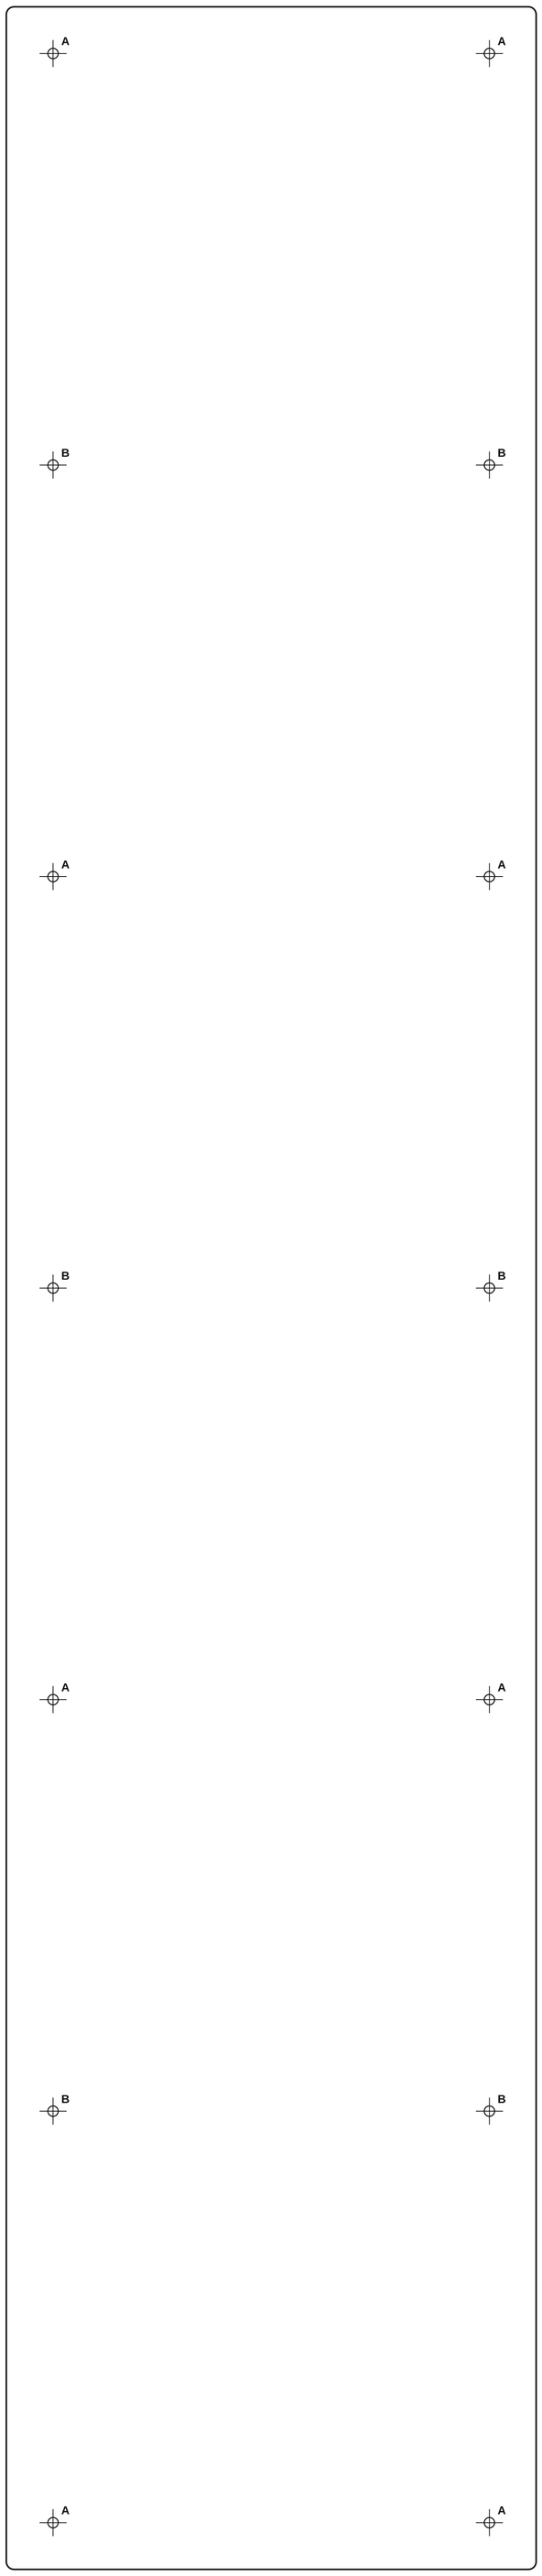

middle — 8.500" × 41.125"

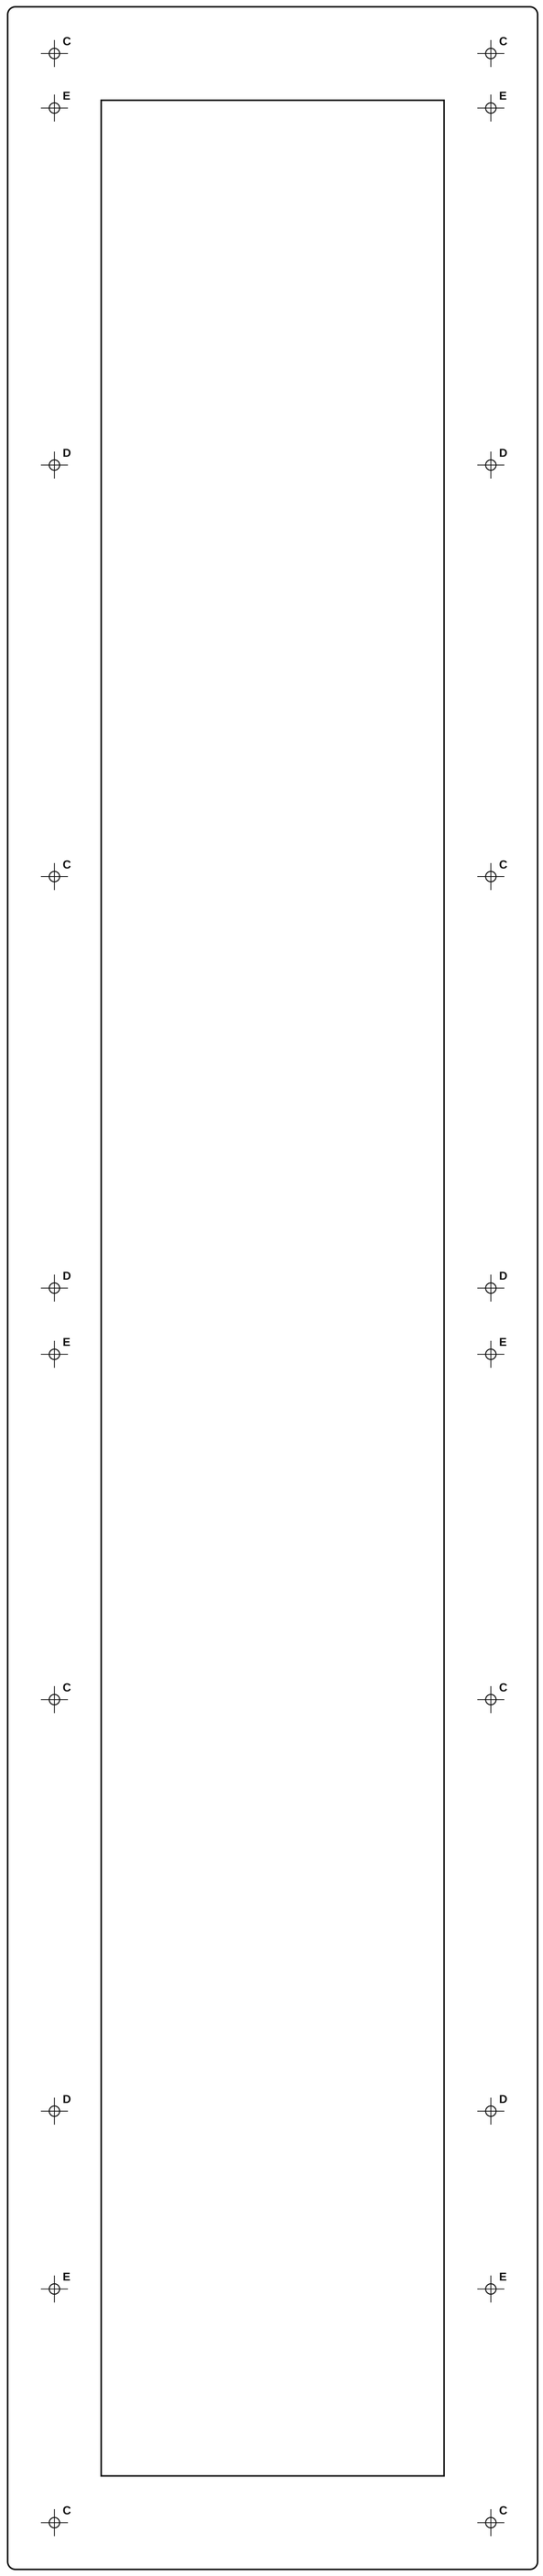

frame (weldment) — 8.500" × 41.125"

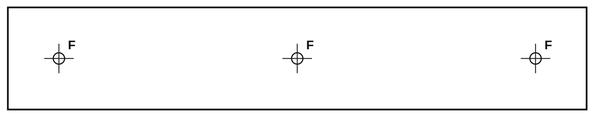

base — LOWER bar, plan view — 8.500" × 1.500"

Drill legend

- **A** drill 11/32" (0.344) — bolt clearance, face+middle (from 1/8" plasma pilot)
- **B** drill 13/64" (0.203) — solid rivet, face+middle (from 1/8" plasma pilot)
- **C** drill 17/64" (0.266) → tap 5/16-18 — frame, 8 places [same bit as B]
- **D** drill 11/32" (0.344) — rivet shop-head relief, frame
- **E** drill 9/32" (0.281) + 82° countersink to 0.500 dia ON THE BACK FACE — Tapcon → brick, frame
- **F** drill 9/16" (0.562) — plug-weld holes, base LOWER bar only

Clamp face+middle and drill A/B pairs together. E countersinks are cut from the BACK (brick side) — heads must finish flush. Plasma pilots are 1/8 nominal.